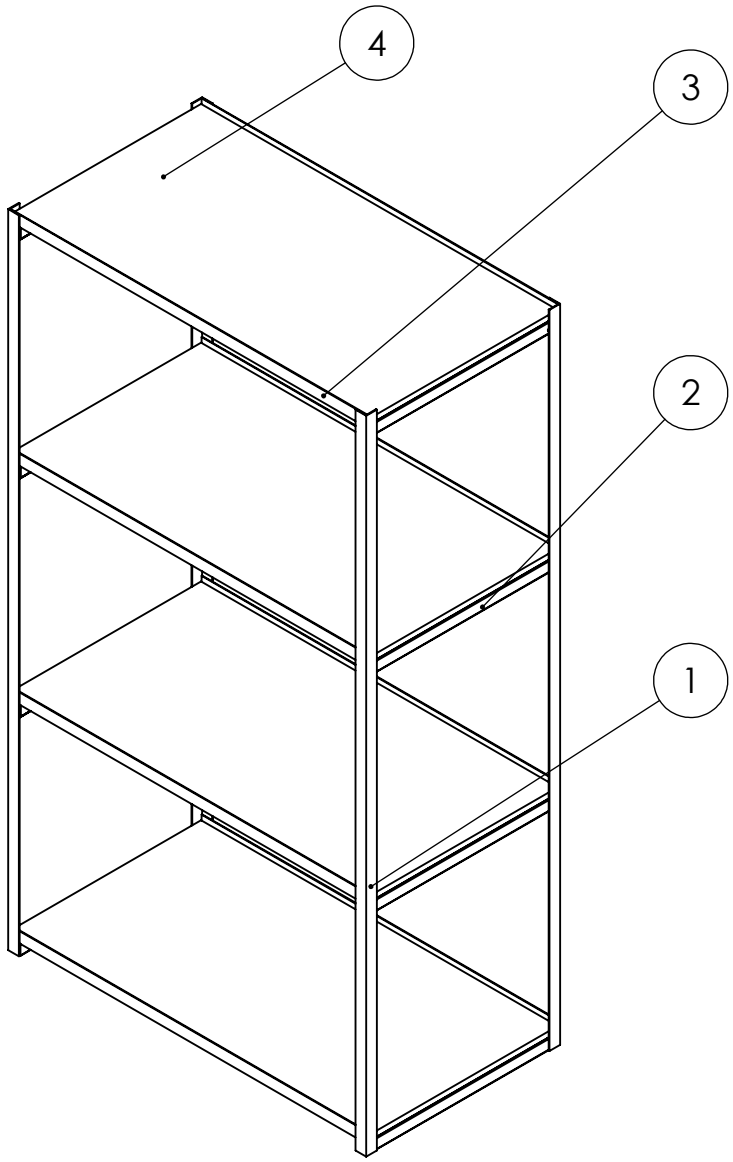

No	Nama Bagian	Bahan	Jumlah	Ukuran	Keterangan
4	Bagian Alas	Multiplek	4	1000 x 535 x 15	
3	Bagian Depan	Besi Siku	8	3 x 3 x 1000	
2	Bagian Samping	Besi Siku	4	3 x 3 x 500	
1	Bagian Penopang	Besi Hollow	8	2 x 2 x 540	

TOLERANSI UMUM
+- 0.1

RAK GUDANG

Skala : 1:15
Satuan : mm
Tanggal : 20-09-2023

Diterima : Bany Abdussalam
Diperiksa : Tesya Permadi
Dibuat : Yulia Nur Rahmatin

KOMPOR UPI

MEGAPROYEK XVI

A4

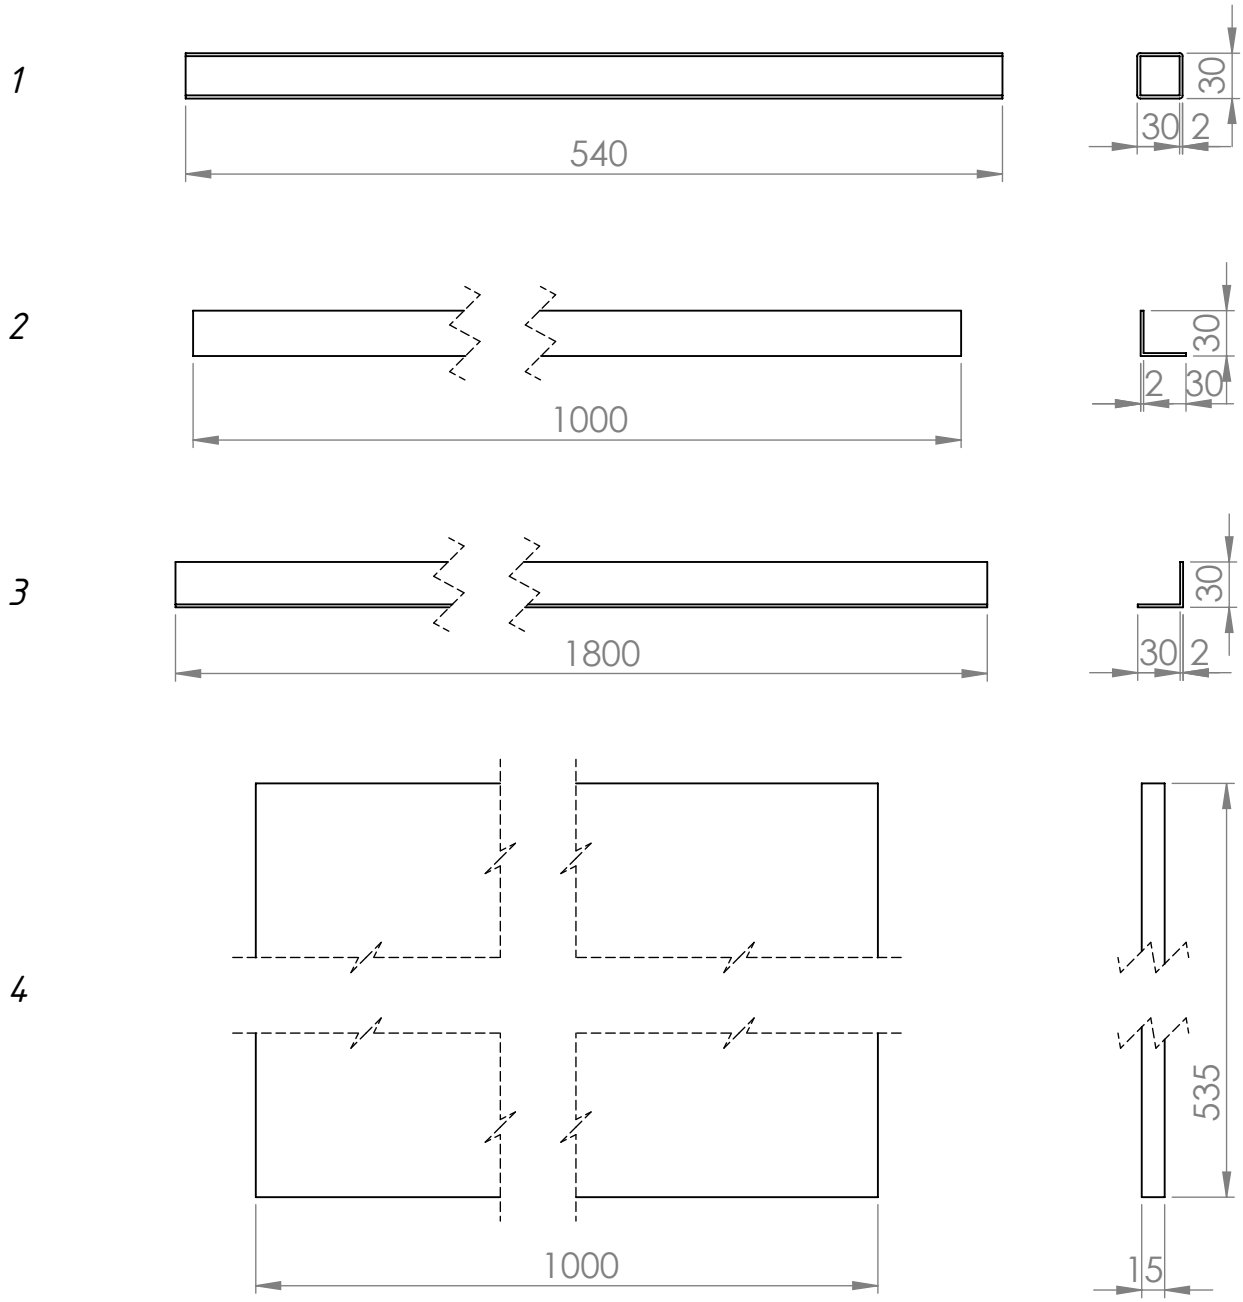

No	Nama Bagian	Bahan	Jumlah	Ukuran	Keterangan
4	Bagian Alas	Multiplek	4	1000 x 535 x 15	
3	Bagian Depan	Besi Siku	8	3 x 3 x 1800	
2	Bagian Samping	Besi Siku	4	3 x 3 x 1000	
1	Bagian Penopang	Besi Hollow	8	2 x 2 x 540	

TOLERANSI UMUM
+- 0.1

RAK GUDANG

Skala : 1:5
Satuan : mm
Tanggal : 20-09-2023

Diterima : Bany Abdussalam
Diperiksa : Tesya Permadi
Dibuat : Yulia Nur Rahmatin

KOMPOR UPI

MEGAPROYEK XVI

A4